

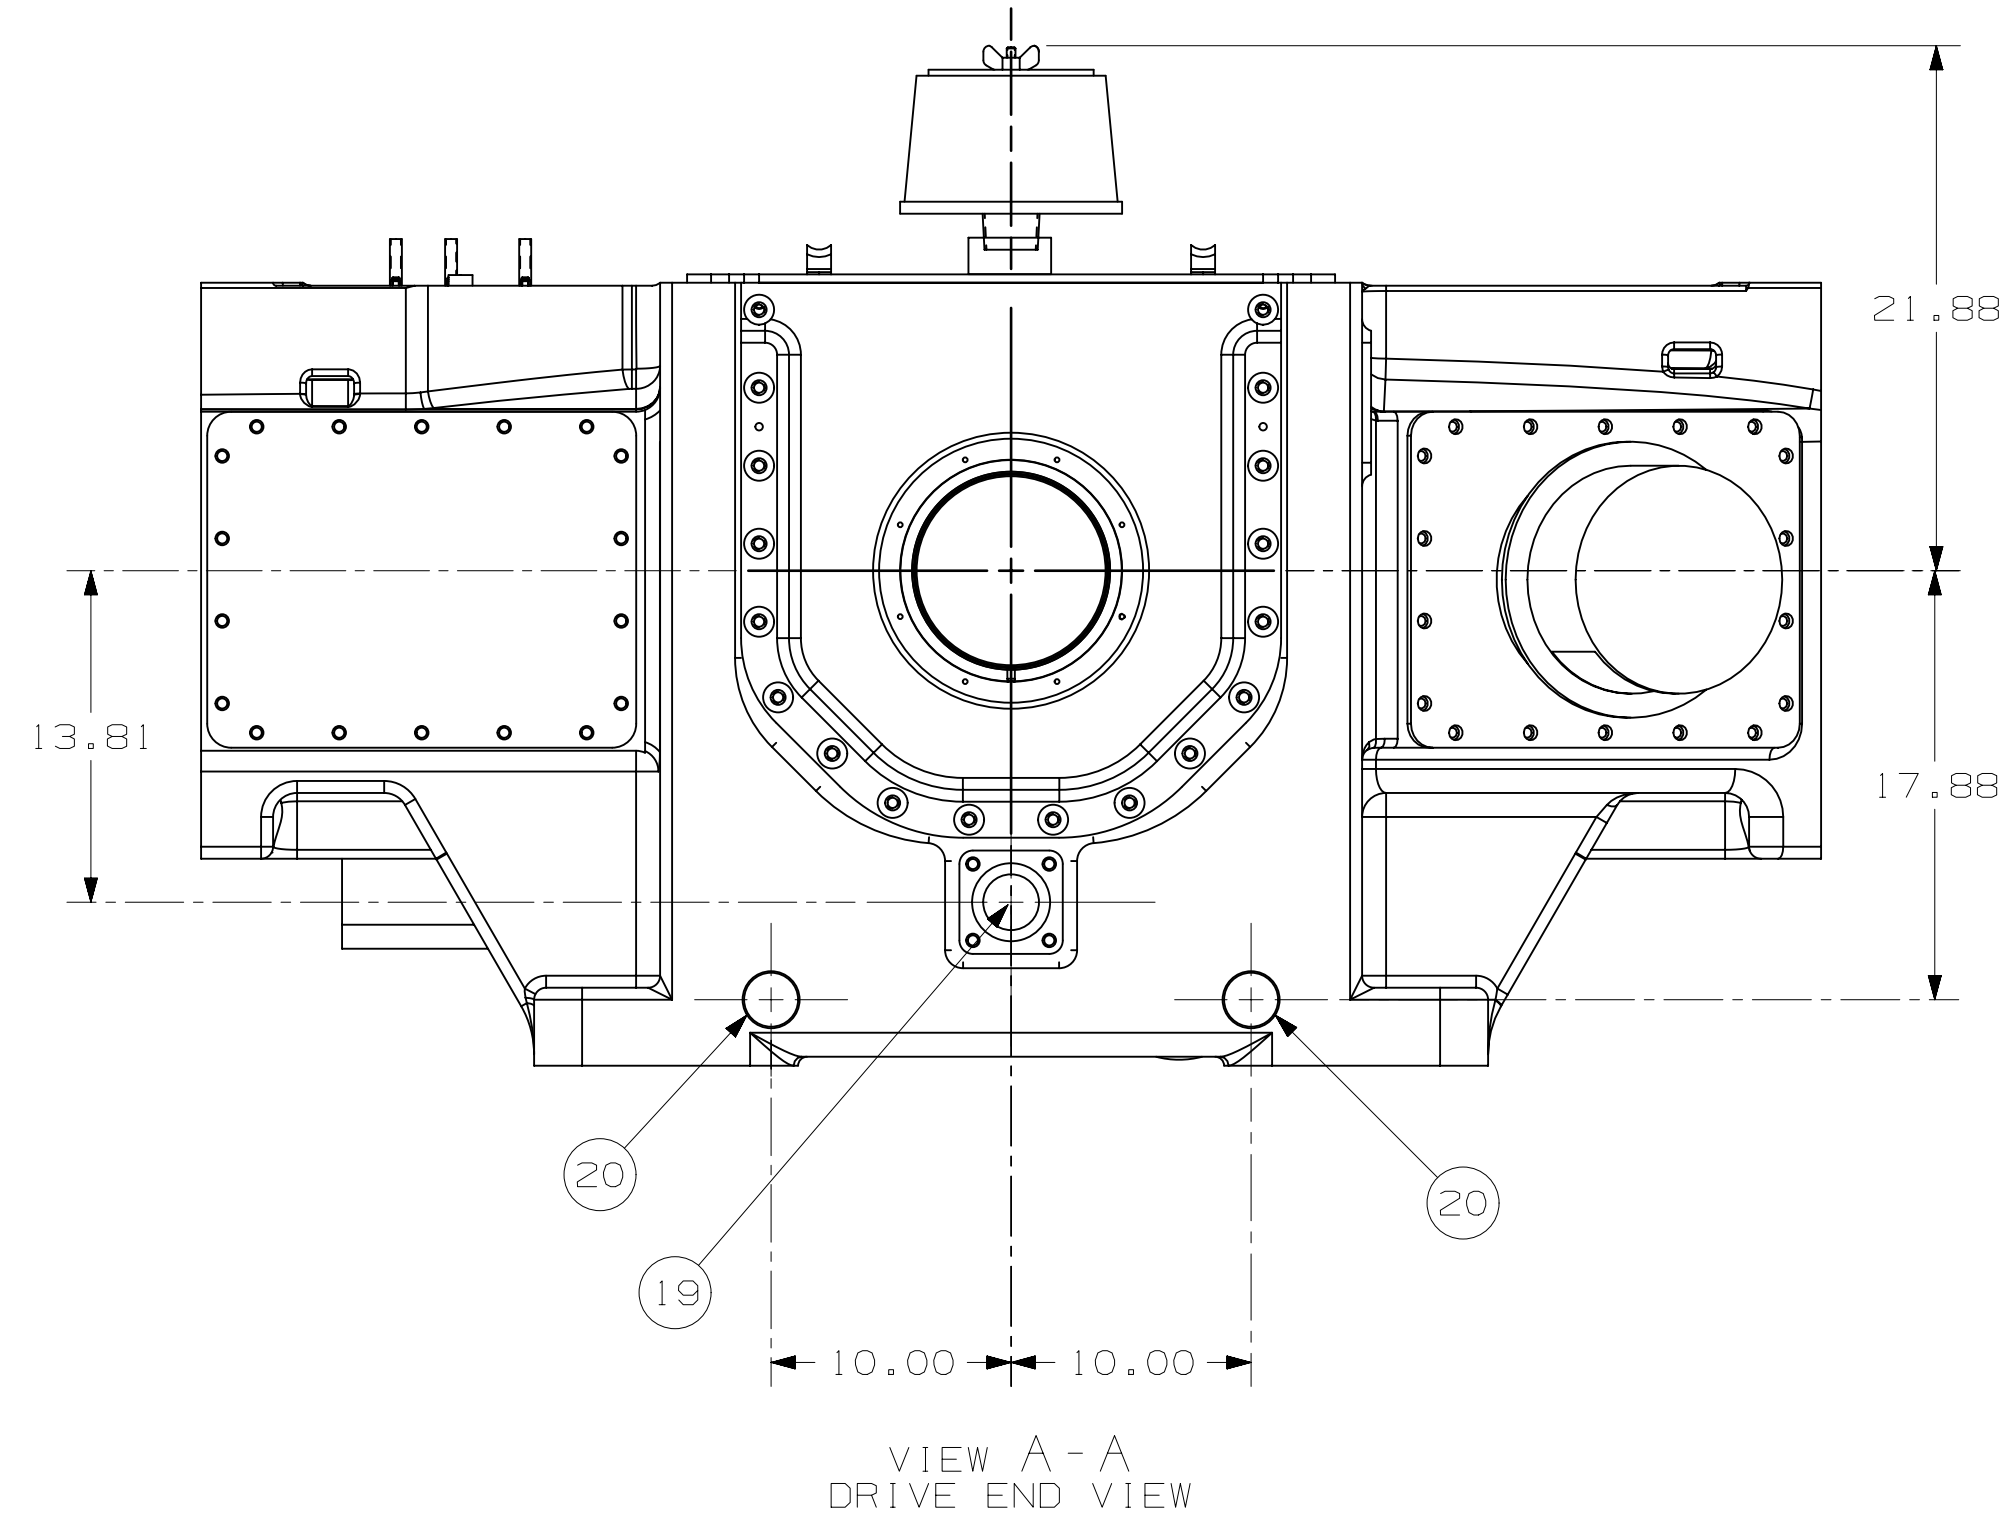
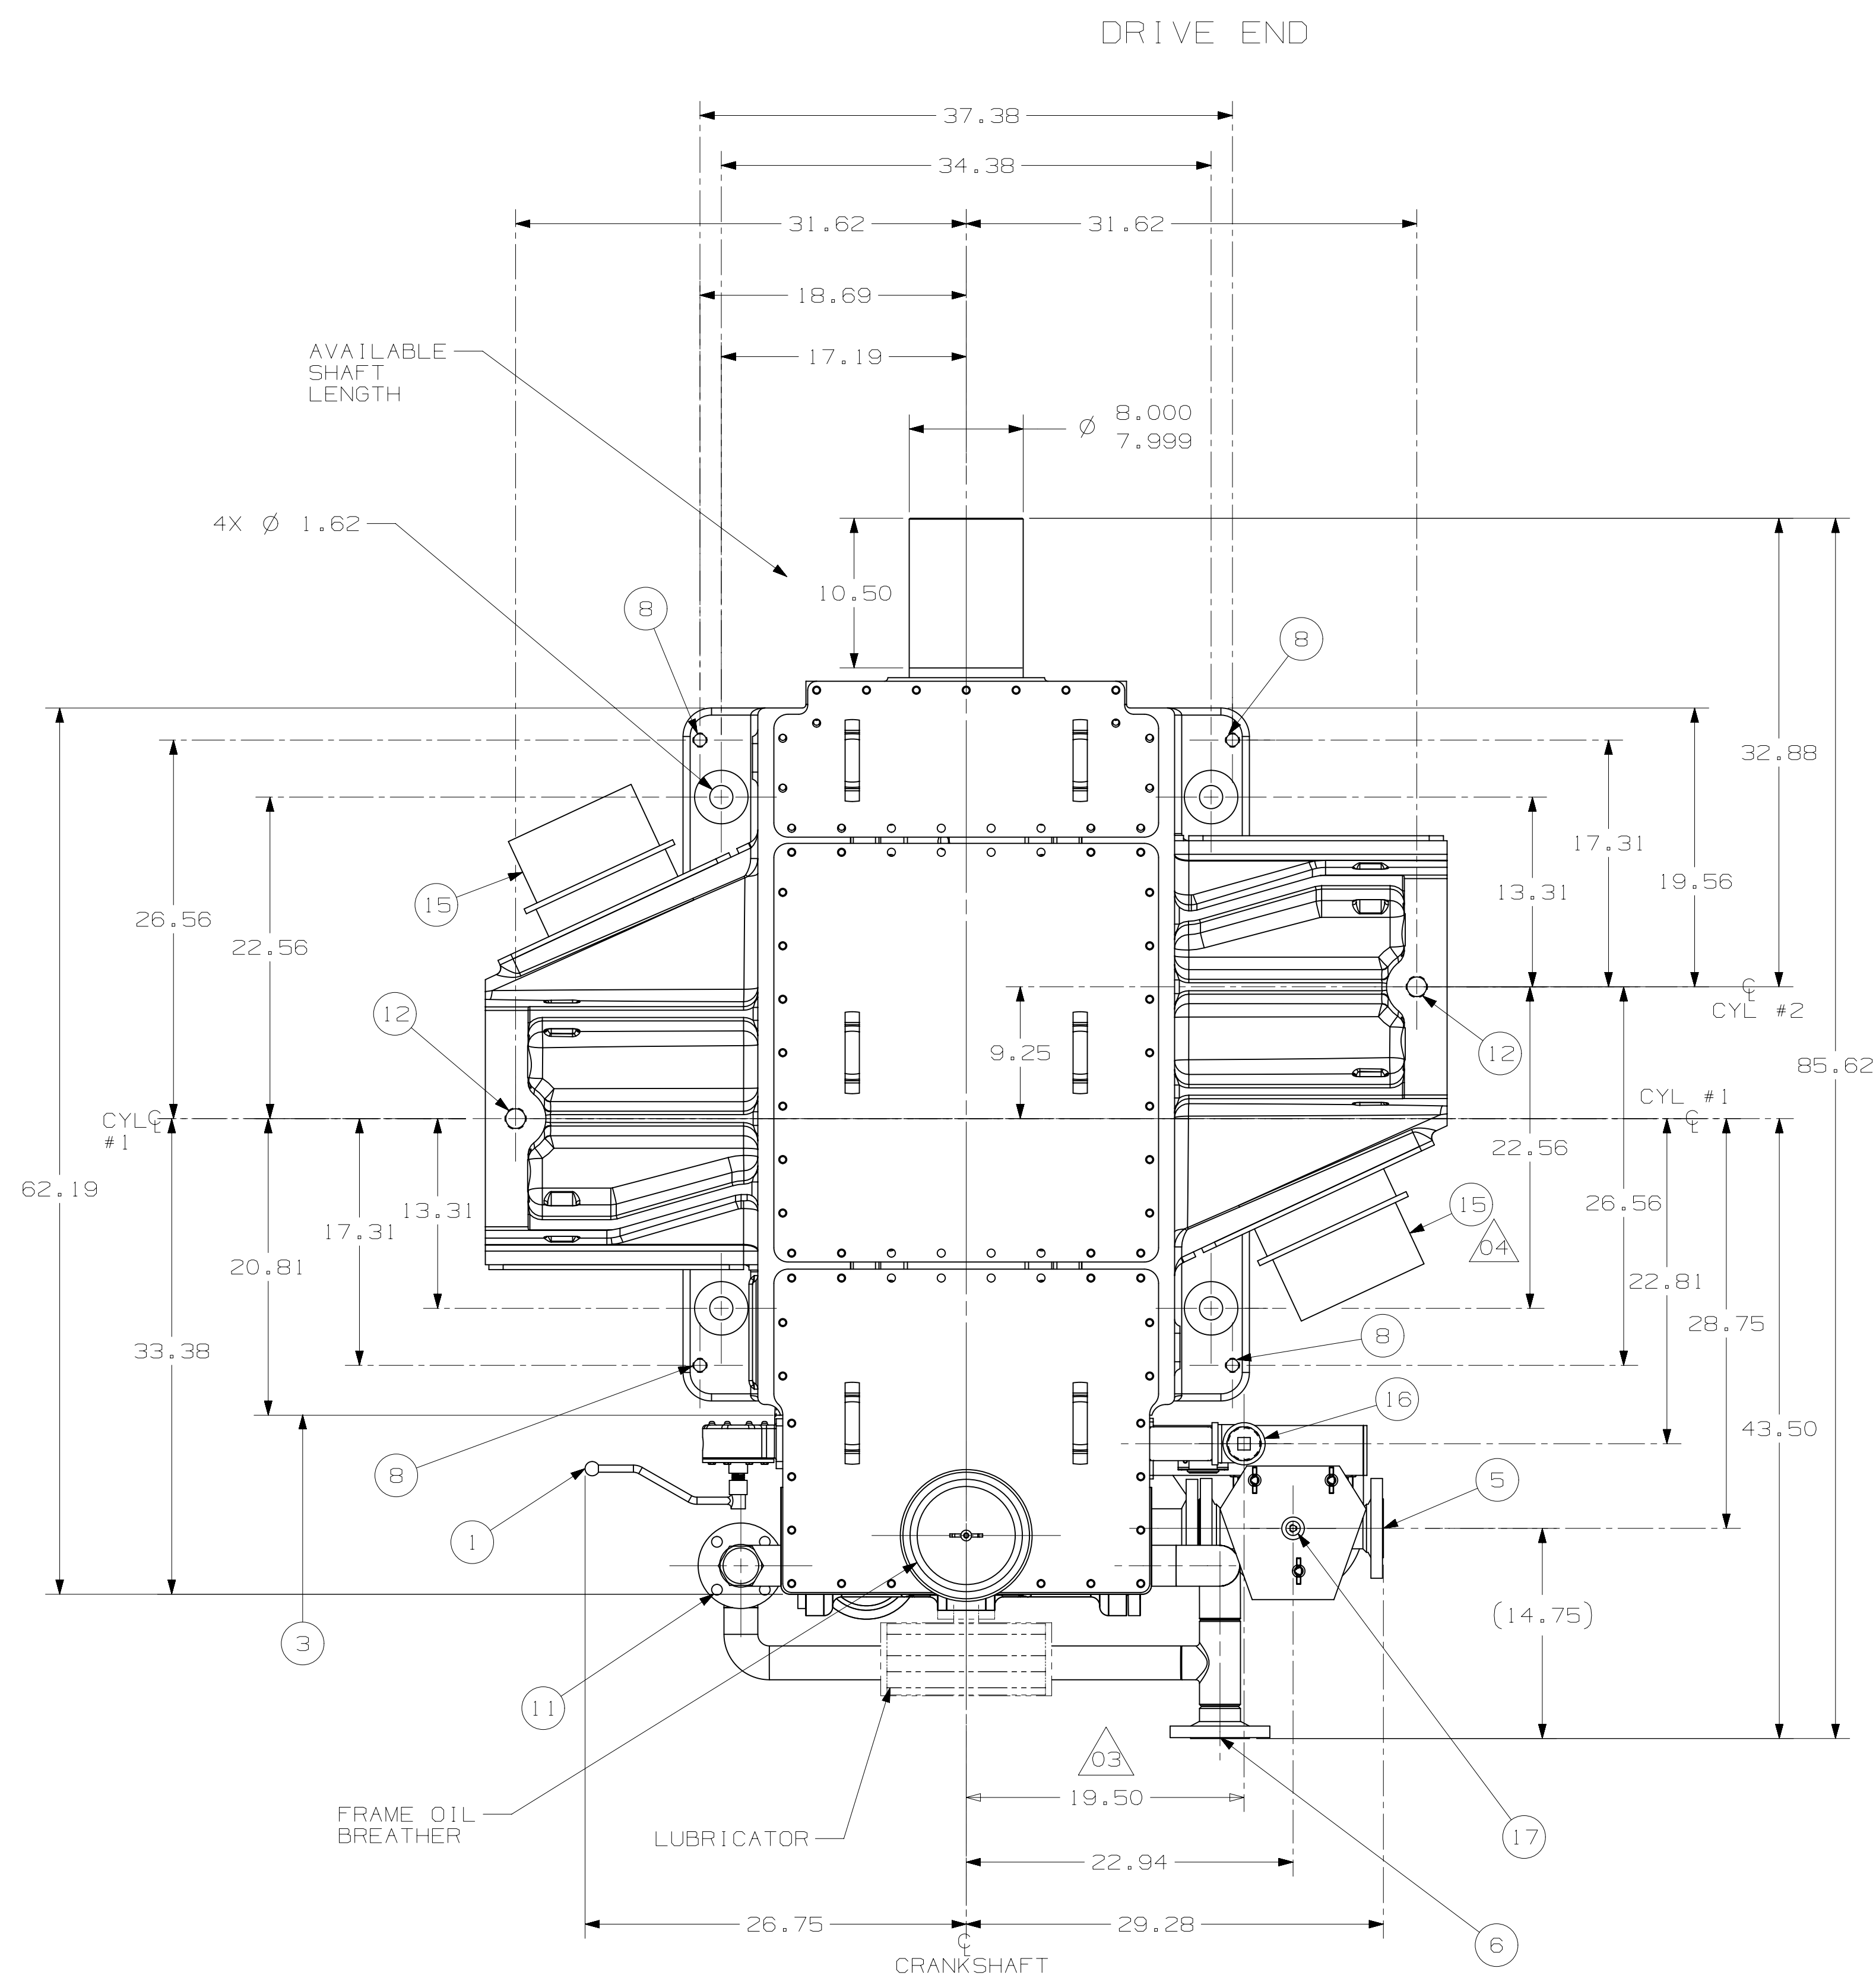


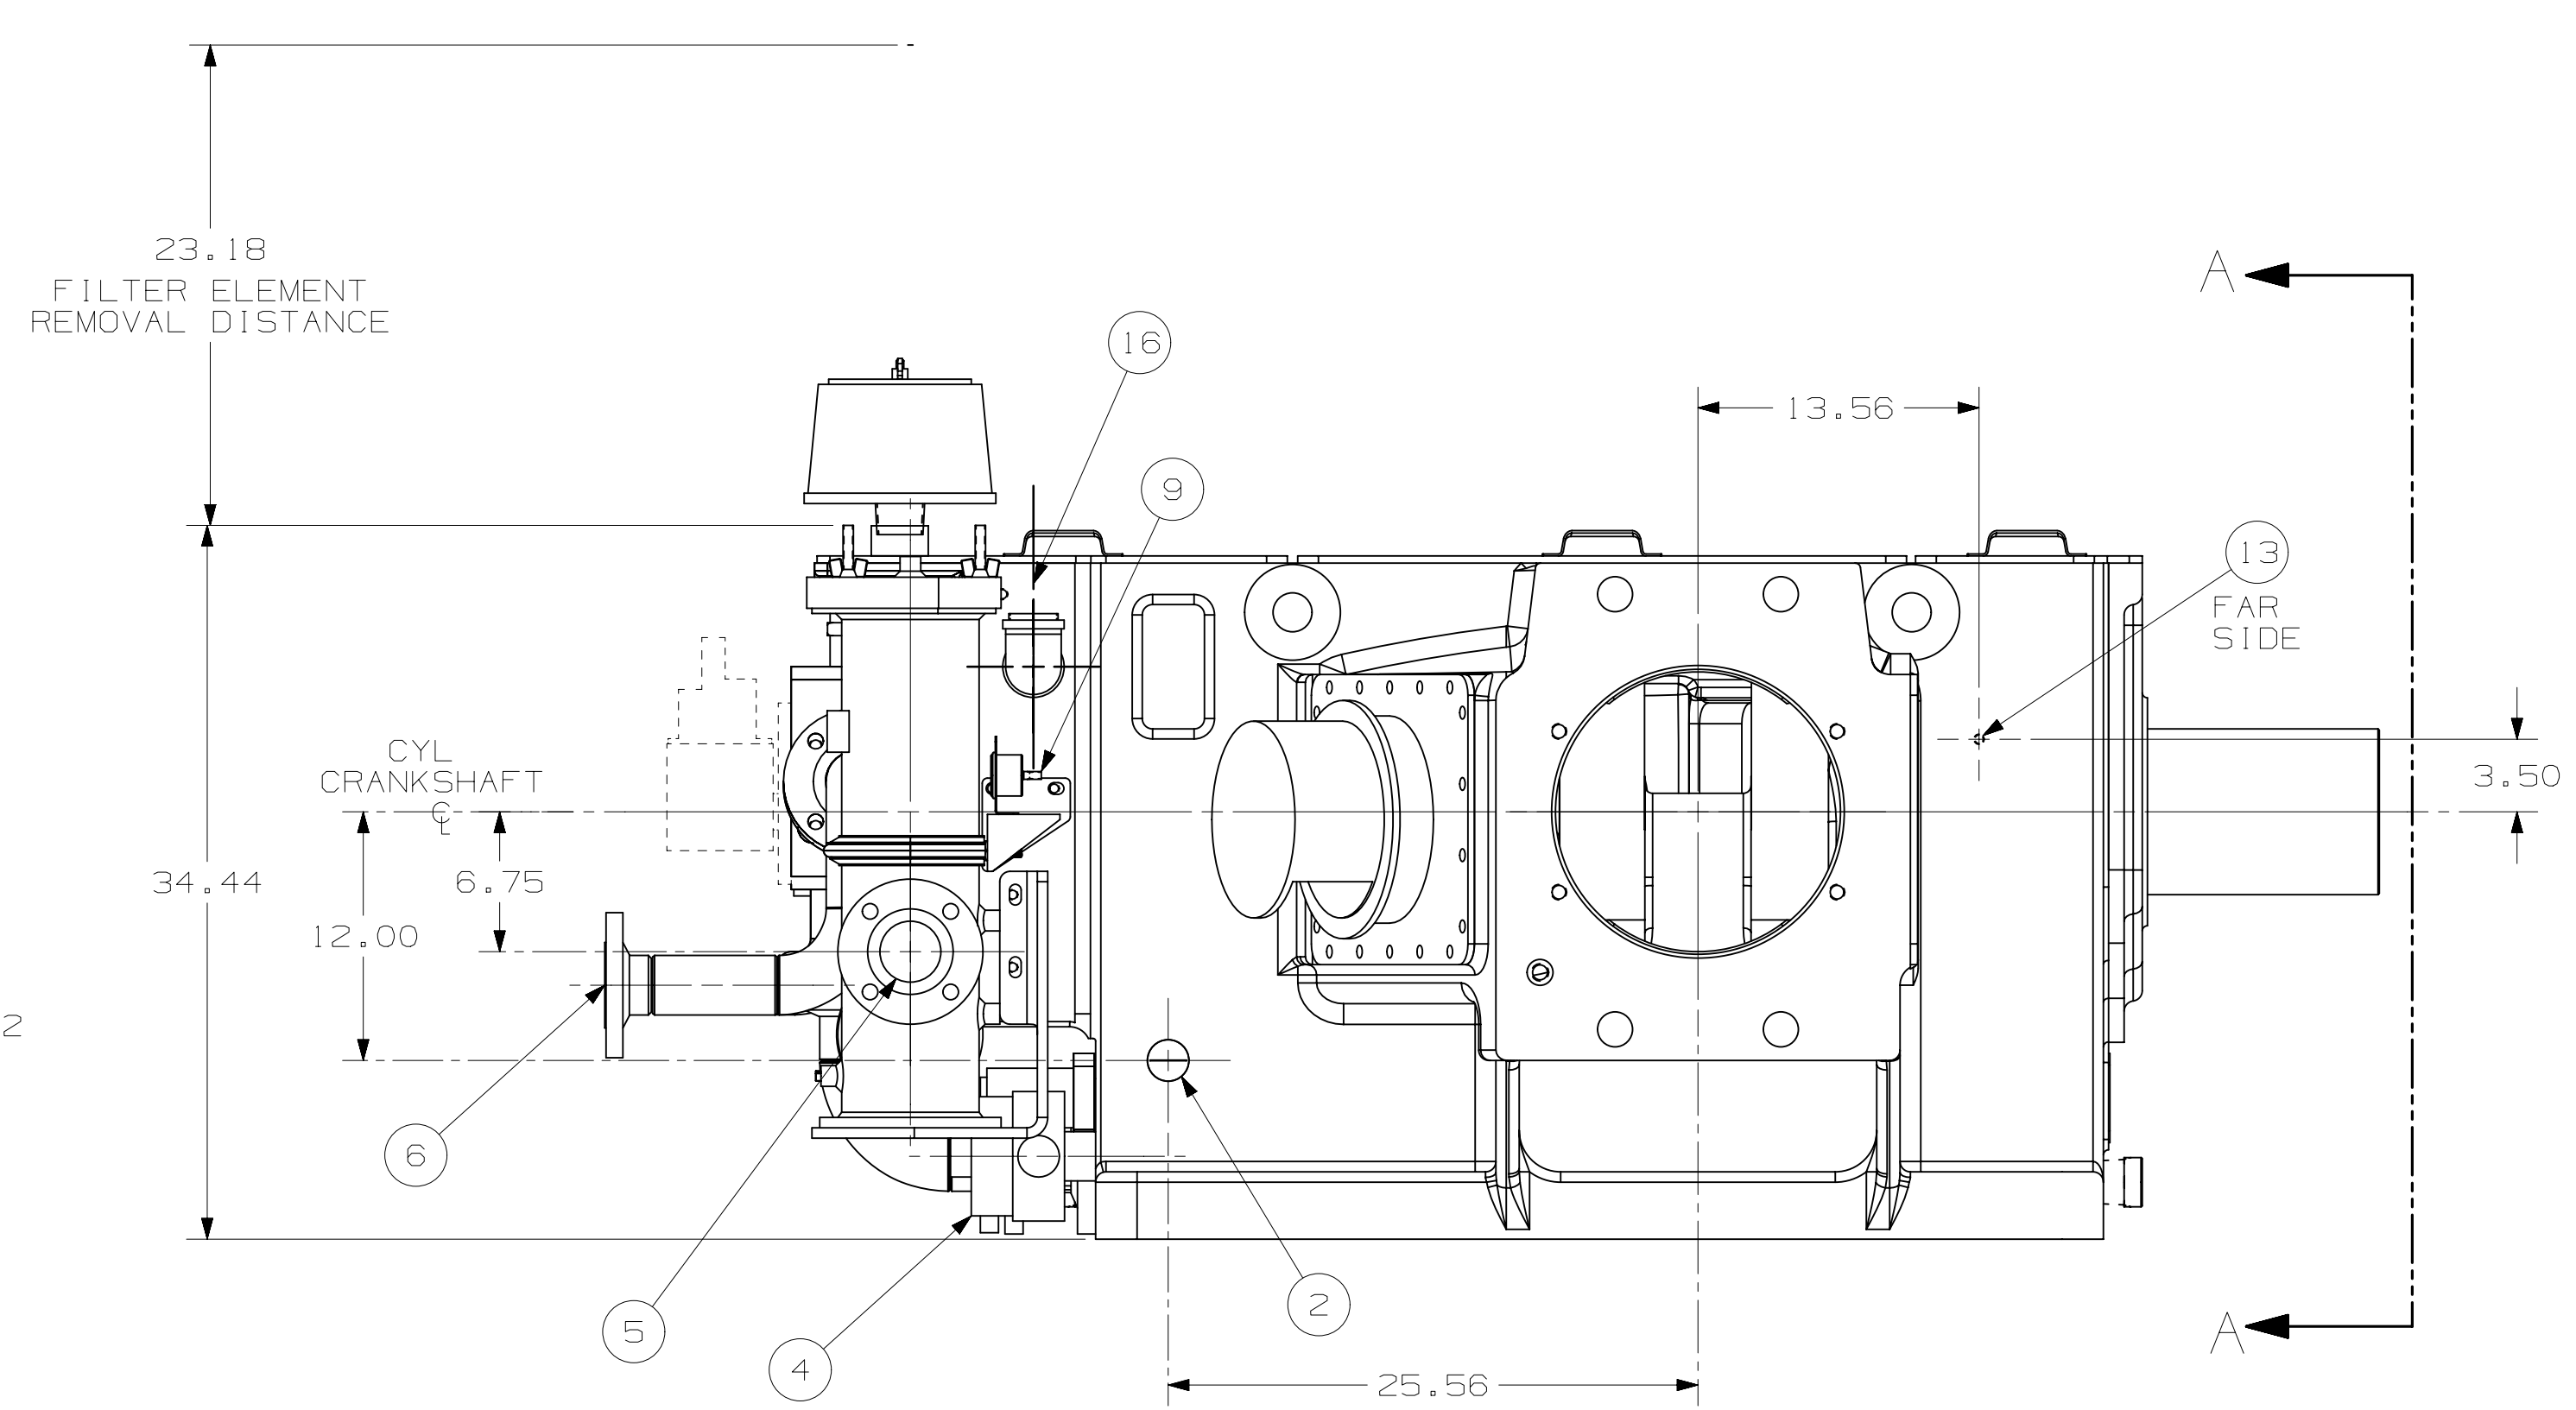

- | | |
|---|--|
| ① HAND OIL PUMP (IF SUPPLIED) | ⑪ OIL PRESSURE REGULATION VALVE - FACTORY SET AT 60 PSIG |
| ② FRAME OIL LEVEL INDICATOR | ⑫ 1.500-BUN-3B THD, 2.25 FULL THD LIFTING LUG. (1 PER THROW) |
| ③ 2.000 NPT - FRAME OIL DRAIN (PLUGGED) | ⑬ .750 NPT RTD - 2 HOLES (IF REQUIRED). |
| ④ FRAME OIL HEATER (IF REQUIRED) | ⑭ .750 NPT - FRAME OIL LEVEL CONTROLLER (IF REQUIRED) |
| ⑤ 2.500 150# RF FLANGE - FRAME OIL INLET FROM COOLER | ⑮ BICERA DOOR - IF REQUIRED BY CLIENT |
| ⑥ 2.500 150# RF FLG - FRAME OIL OUTLET TO COOLER | ⑯ 2.000 NPT - FRAME OIL FILLER |
| ⑦ .750 NPT AUXILIARY LUBE CONN - (PLUGGED) | ⑰ .250 NPT - OIL FILTER VENT/PURGE CONN |
| ⑧ LEVELING SCREWS 1.000-BUNC-3B THD | ⑱ .750 NPT - OIL FILTER DRAIN PORT CONN |
| ⑨ OIL FILTER DIFFERENTIAL PRESSURE INDICATOR (D-R CO. TO FURNISH) | ⑲ .125 NPT - MAIN BRG OIL HEADER PRESS CONN (CUSTOMER CONN) |
| ⑩ .750 NPT - OIL LEVEL CONTROL VENT (PLUGGED) | ⑳ 2.000 NPT - DRY-SUMP CONNECTION - PLUGGED. |
| | ㉑ .500" NPT THD LUBRICATOR VENT/OVERFLOW (IF REQUIRED) |
| | ㉒ LUBRICATOR OIL SUPPLY (1.25 NPT) |

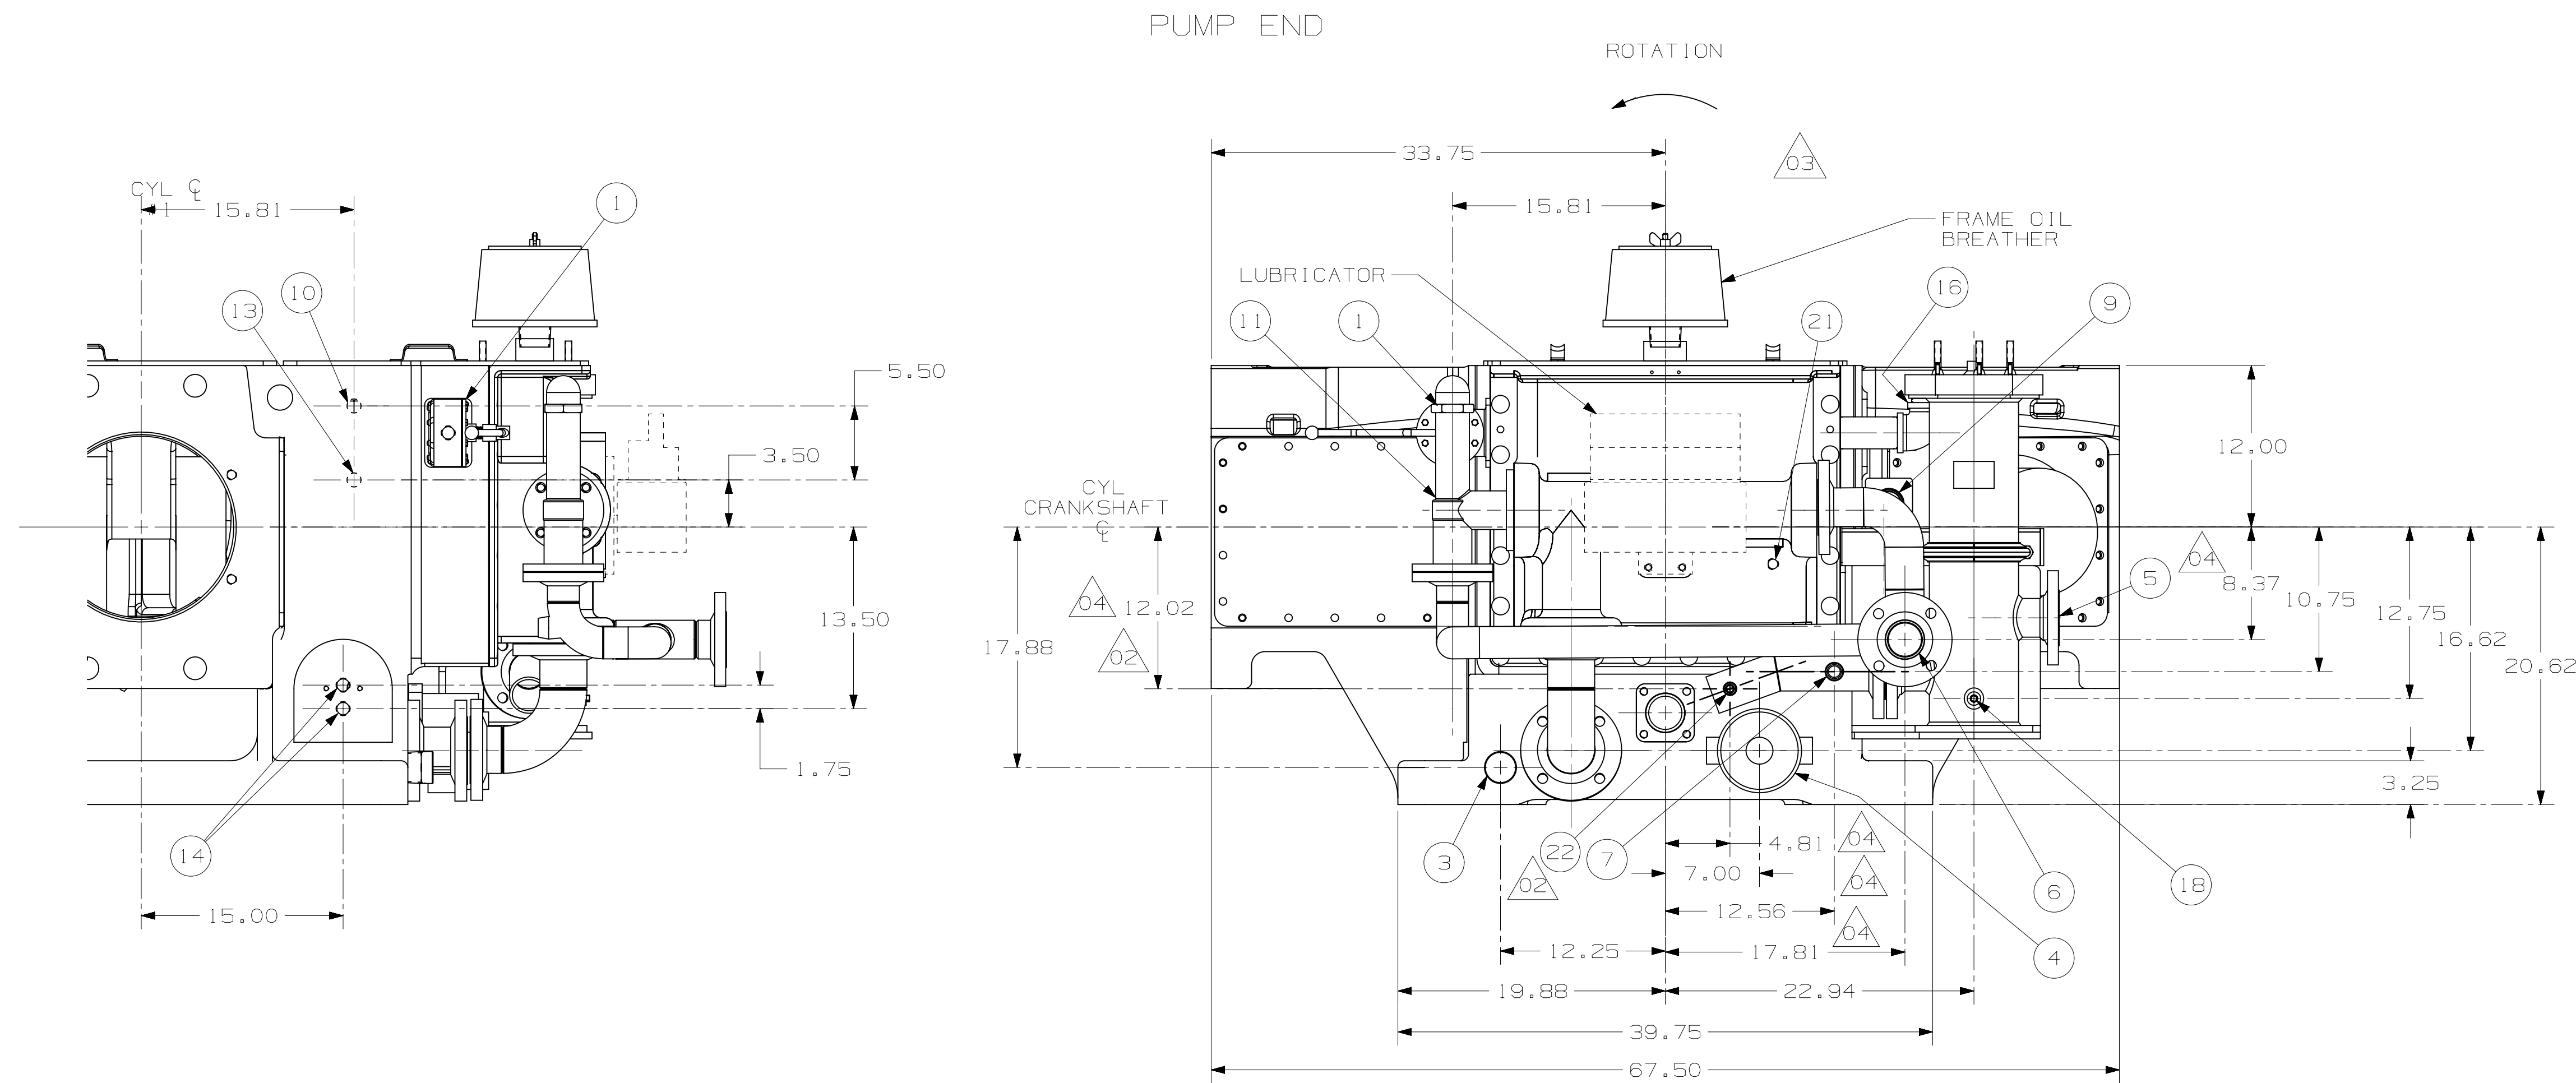

TOTAL APPROX WEIGHT: 8,700 LBS

SIZE			STROKE			TYPE		
35.000			617			HOSS		

REV	DRAWN BY/DATE	CHECKED BY/DATE	APPROVED BY/DATE	DESCRIPTION OF CHANGE
06	M. CORWIN	S. DIBSD	S. SEVEY	UPDATED DRAWING SHEET TO CURRENT
05	S. DIBSD	S. DIBSD	S. DIBSD	SAP TRANSFER ERROR
04	ESK	ESK	ESK	DRN 12.02 WAS 11.91 4.81 WAS 5.06 12.56 WAS 12.06 17.81 WAS 16.25 8.37 WAS 7.38 BICERA DOOR QTY 2 WAS 1 ESC/SWPNL
03	KMD	KMD	SAB	REMOVED 15.56 DIM. ADDED 19.50 DIM. EEN080376. KMD
02	CWG	CWG	GFB	ADDED CONN NO. 22 ECM 080070
01	DL SYMONS	DL SYMONS	DAB	ADDED LUBE VENT CONN. ILL 21 080078
00	DL SYMONS	DL SYMONS	DAB	

DATE	NAME	SCALE	TYPE
8/15/06	EJMCCOY	1/25	outline drawing
8/28/06	OFB1SEL		

DATE	NAME	SCALE	TYPE
2/28/07	TEBLAZEJEWSK		

DATE	NAME	SCALE	TYPE
8/15/06	EJMCCOY	1/25	outline drawing
8/28/06	OFB1SEL		

DATE	NAME	SCALE	TYPE
2/28/07	TEBLAZEJEWSK		

